


LOCATION_Thane, India

INOX

Design Company_Arris Architects Pvt Ltd
Area_1,300m^2
Photographer_INOX Leisure Ltd, Ajinkya Manohar


The principle attempt for the design was to break away from the conventional format of following the slopes of the cinemas, in turn bringing about a new brand identity for INOX. Cinema panel design interprets the side façade as a wall piece that would give a pleasant visual experience for the patrons at time of entering the cinema and intermission, while at the same time not bold enough to distract during movie watching. The wall skin is a blend of different colors in a drape form, at the same time making the design more time and cost effective. Design revolves around the concept of contemporary, vibrancy, playfulness, and optical illusions. The layering of colors juxtaposed within the main colors lends the skin a varied appearance, which is vivid and three dimension from close-up and appears homogeneous and flat from far. The colorful stripes design pattern is aptly concise in the ribbony drapes which are held within the brown fabric paneling. Interior space of concession lobby is an extension of the same concept though more like a prologue to it. The lobby space is inscribed in an inclined elliptical shell, increasing its effective volume & detaching itself from the direction expression of structural slopes. The use of mirrors on beams makes the huge structural beams disappear & brings lightness to the space. It uses the identical stripe pattern in a more subtle way. Wall cladding in vitrified tiles with a monochromatic pattern identifies itself with cinema design. Concession counter shell displays a white shell running throughout the linear interior space and caving in at places with bright yellow cross sections for counters and auditorium entries. Flooring of silver travertine along with inlays of white agglomerated marble flows through the linear space. The same lines extrude themselves to form seating enclave. Front graphic wall & pattern in the ceiling add vibrancy to the space. The entire space displays various elements each expressing their individuality, however bound together by a central concept and detailing, thus forming an integral space with variety of experiences justifying its concept.


RESTROOMS

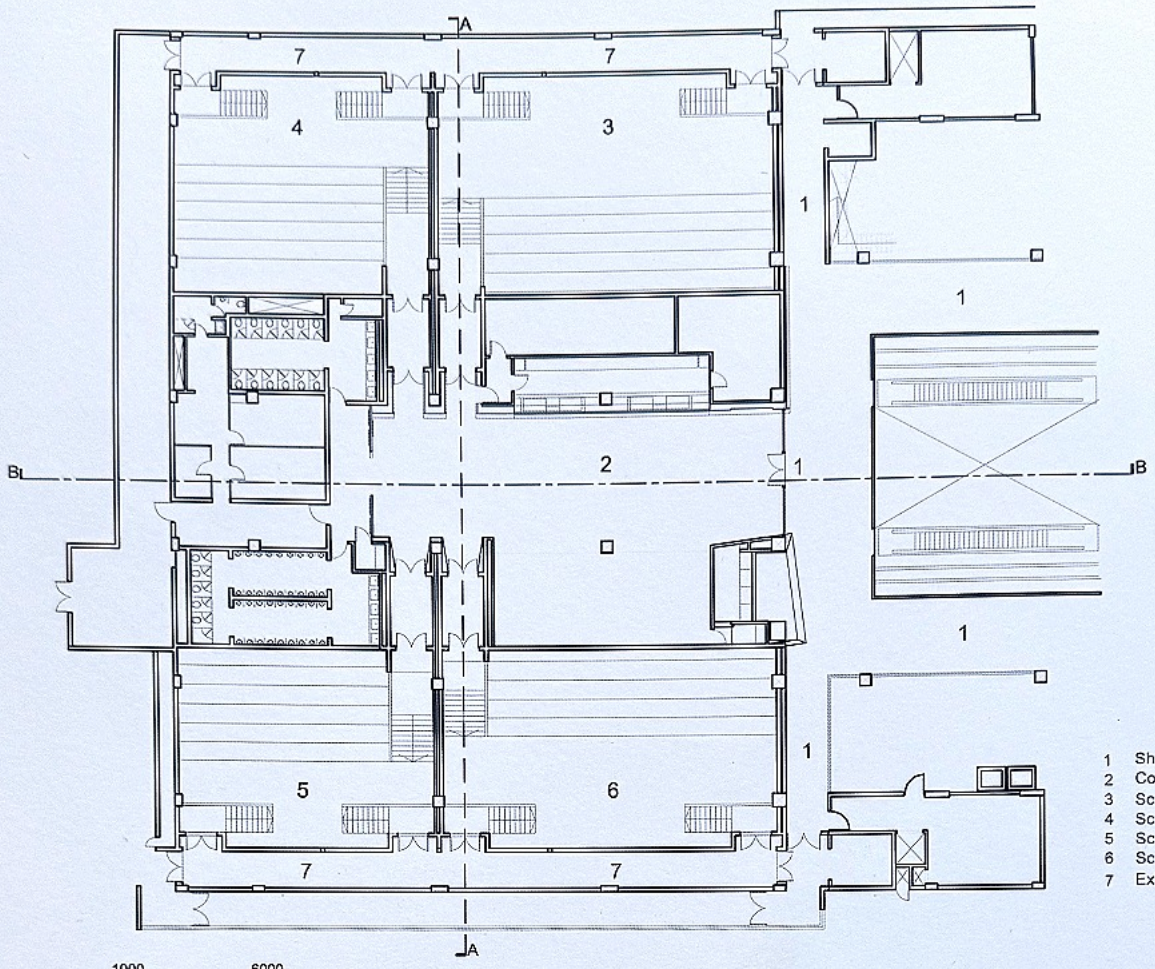

THIRD FLOOR PLAN

Korum Mall,Thane, Maharashtra, India

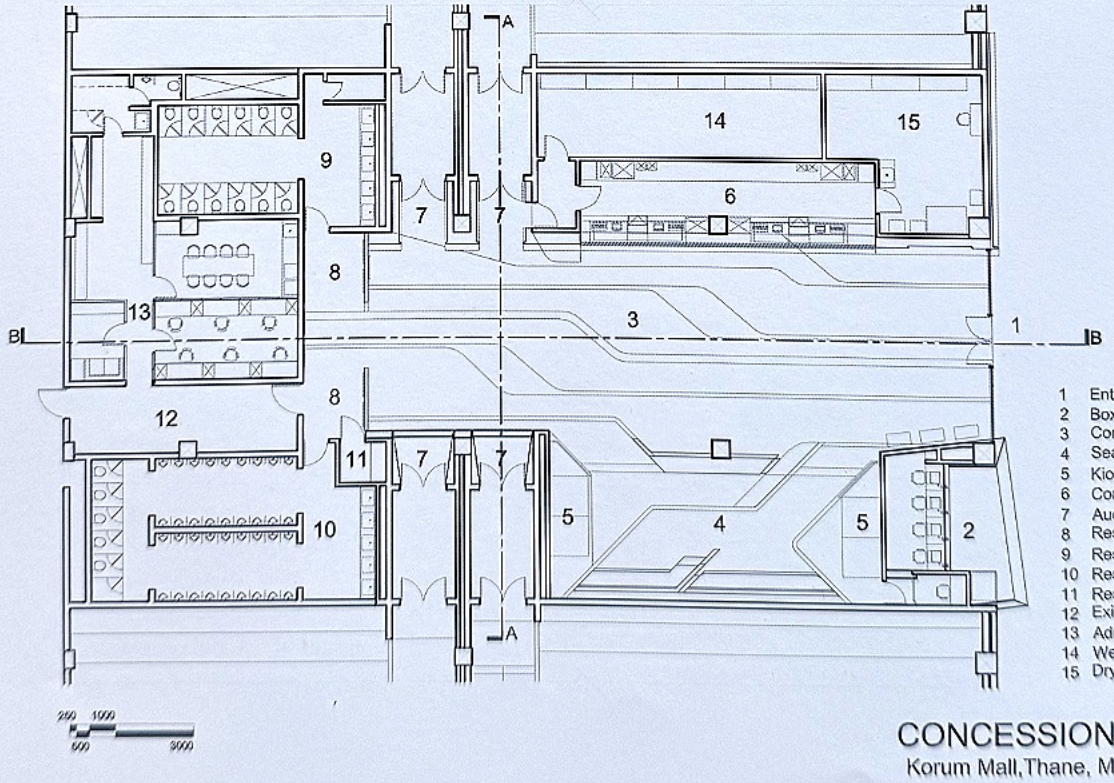


CONCESSIONS LAYOUT


Korum Mall,Thane, Maharashtra, India

Transverse Section AA

Korum Mall,Thane, Maharashtra, India

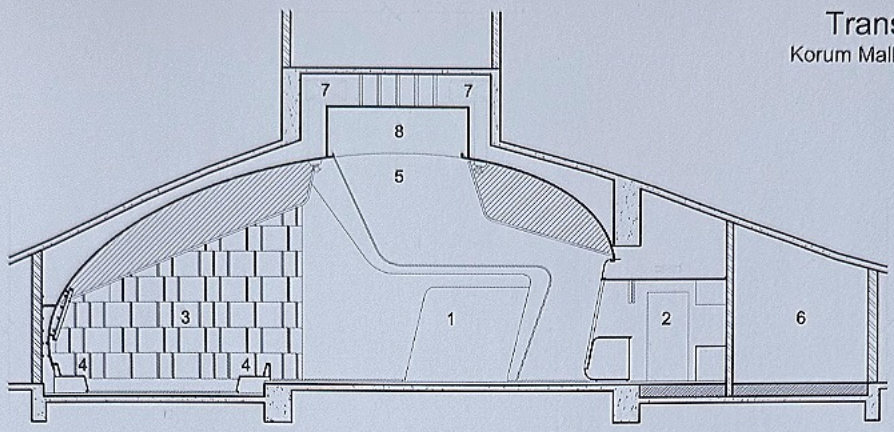

1 Concessions Lobby
2 Concession Counter
3 Wall Cladded in Vitrifed Tile pattern
4 Seating Area
5 Graphic Wall
6 Store Area
2 HVAC Duct
3 Mirror Finish ACP

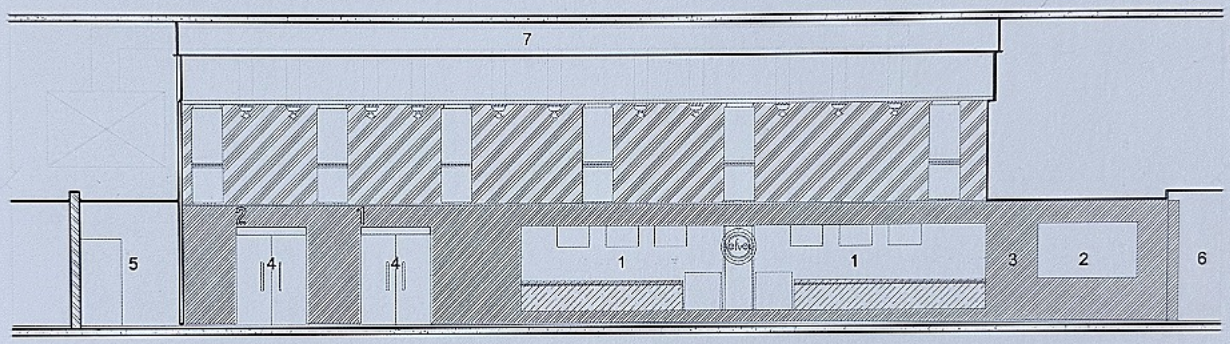



1 Concessions Counter
2 Commercial Signage
3 Shell Finished in White Laminate
4 Auditorium Entrace
5 Restroom Lobby
6 Shopping Mall Corridor
7 HVAC Duct


Longitudinal Section BB


Korum Mall,Thane, Maharashtra, India

这项设计的主要目的是脱离传统影院的斜坡式造型，赋予 INOX 新的品牌形象。经设计，影院侧面的墙片能让观众在进入影院和幕间休息时拥有愉快的视觉效果，同时侧墙也不会因为过于醒目而分散观众观看影片时的注意力。彩色的墙皮呈褶皱状，使设计更加经济高效。设计围绕现代、活力、娱乐和幻觉展开，颜色层次与主色彩相融，增添了墙皮外观的多样性。近距离看，生动而有三维效果；远观时则是二维的平面效果。彩色的条纹图案巧妙地突出了隐藏在棕色墙体中的彩虹图形。贵宾室的内部空间与其说是本次设计主题的序曲，不如说是对主题的延伸。休息室形状似一个椭圆形的贝壳，这样的设计增强了室内的音效，同时也使这个空间摆脱了斜坡式结构的表现形式。横梁上安装的镜子使巨大的横梁在得以通形的同时又将光线引入影院。设计巧妙地运用了同样的条纹图案达到了奇妙的效果。琉璃瓦在墙壁上拼出一个单一的图案与影院设计完美契合。线性的室内空间里，明黄色交叉区标示出前台和礼堂入口，其间坐落着形似白色贝壳的贵宾室。银灰洞石地板与镶嵌于其上的白色人造石穿流在这个线性空间中。线条凸起的部分则成为观众席。前方富有动感的墙体和天花板图形为影院增添了生机。整个空间展示出了多种元素，每种元素都有其独特性，却又通过一个核心主题和设计细节紧密地联系在一起，即以不同的体验搭建起一个整体空间。

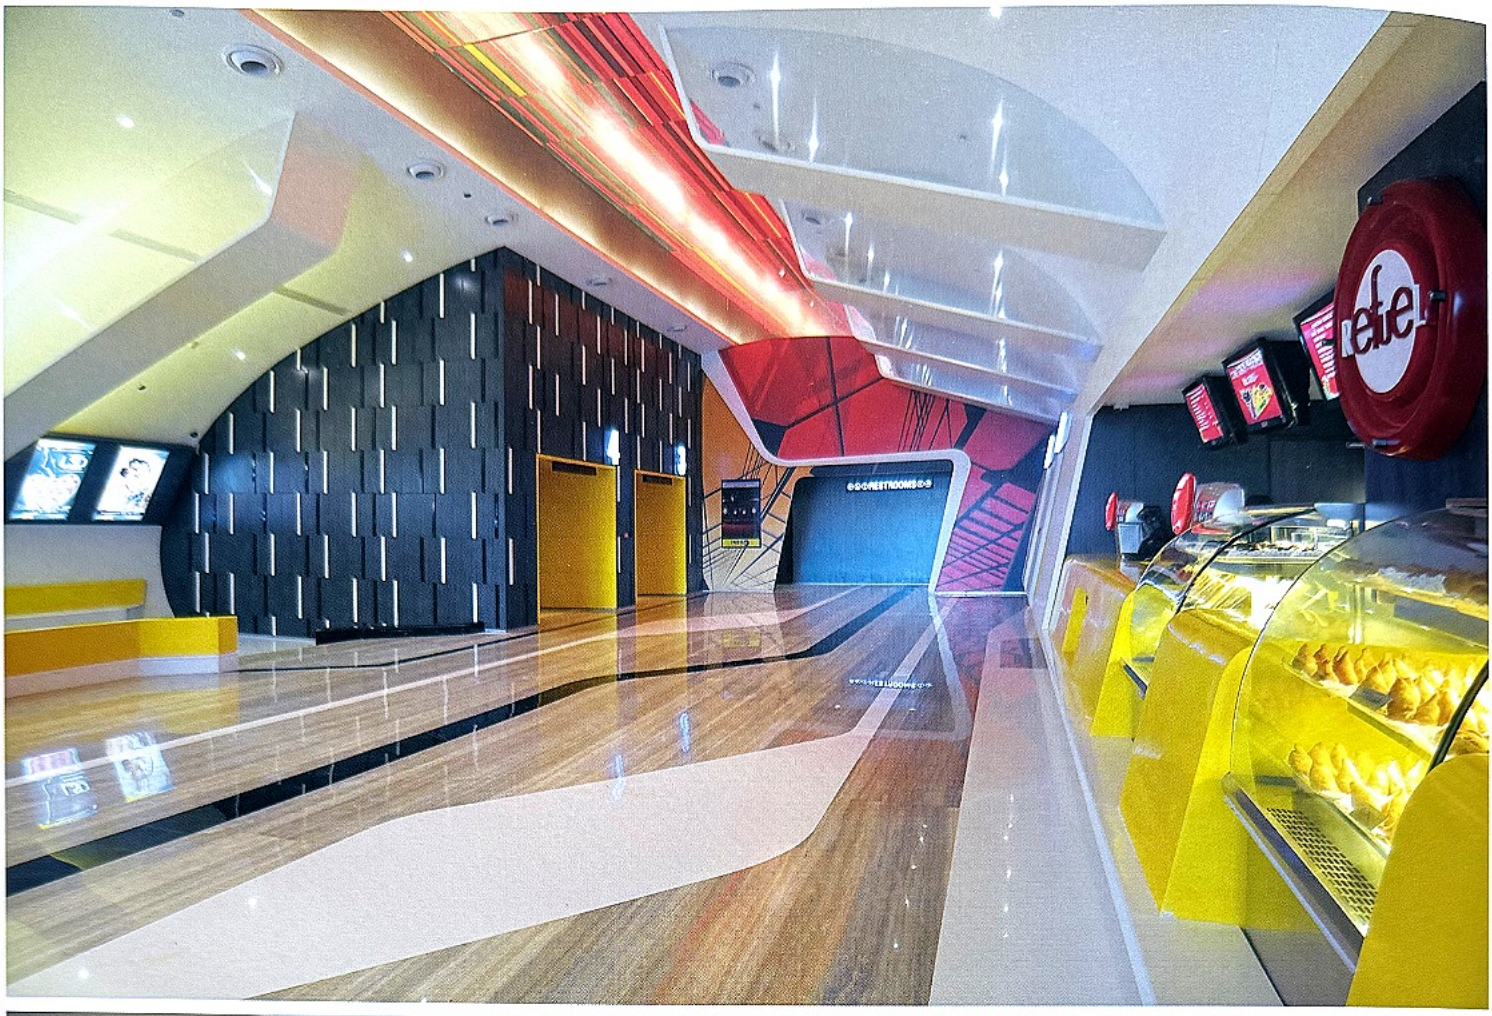

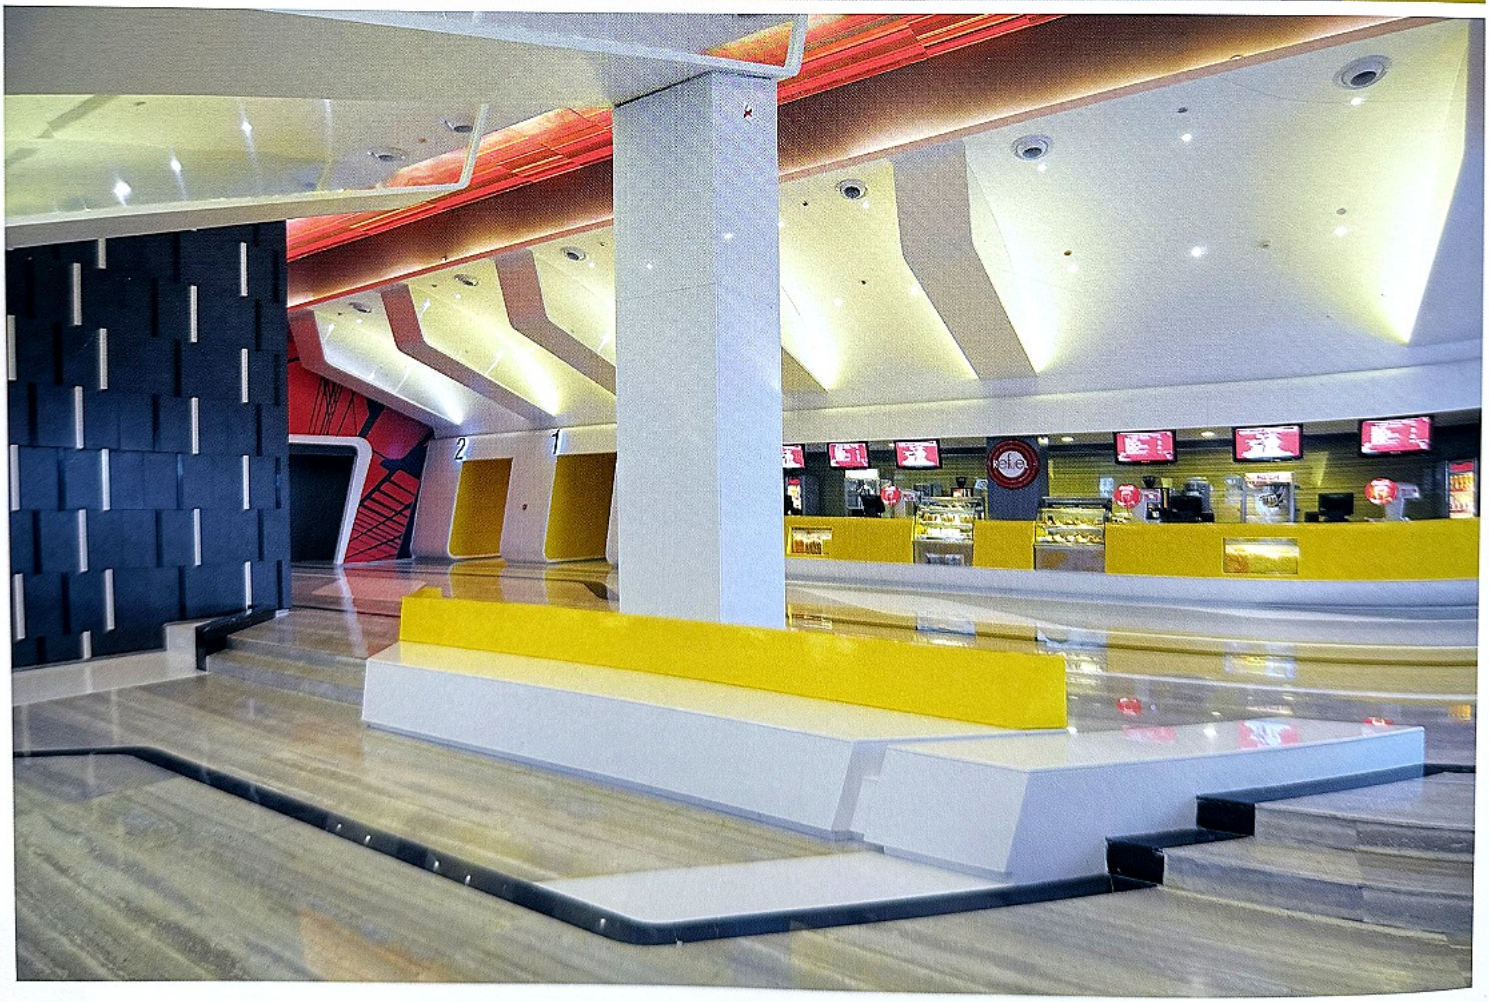

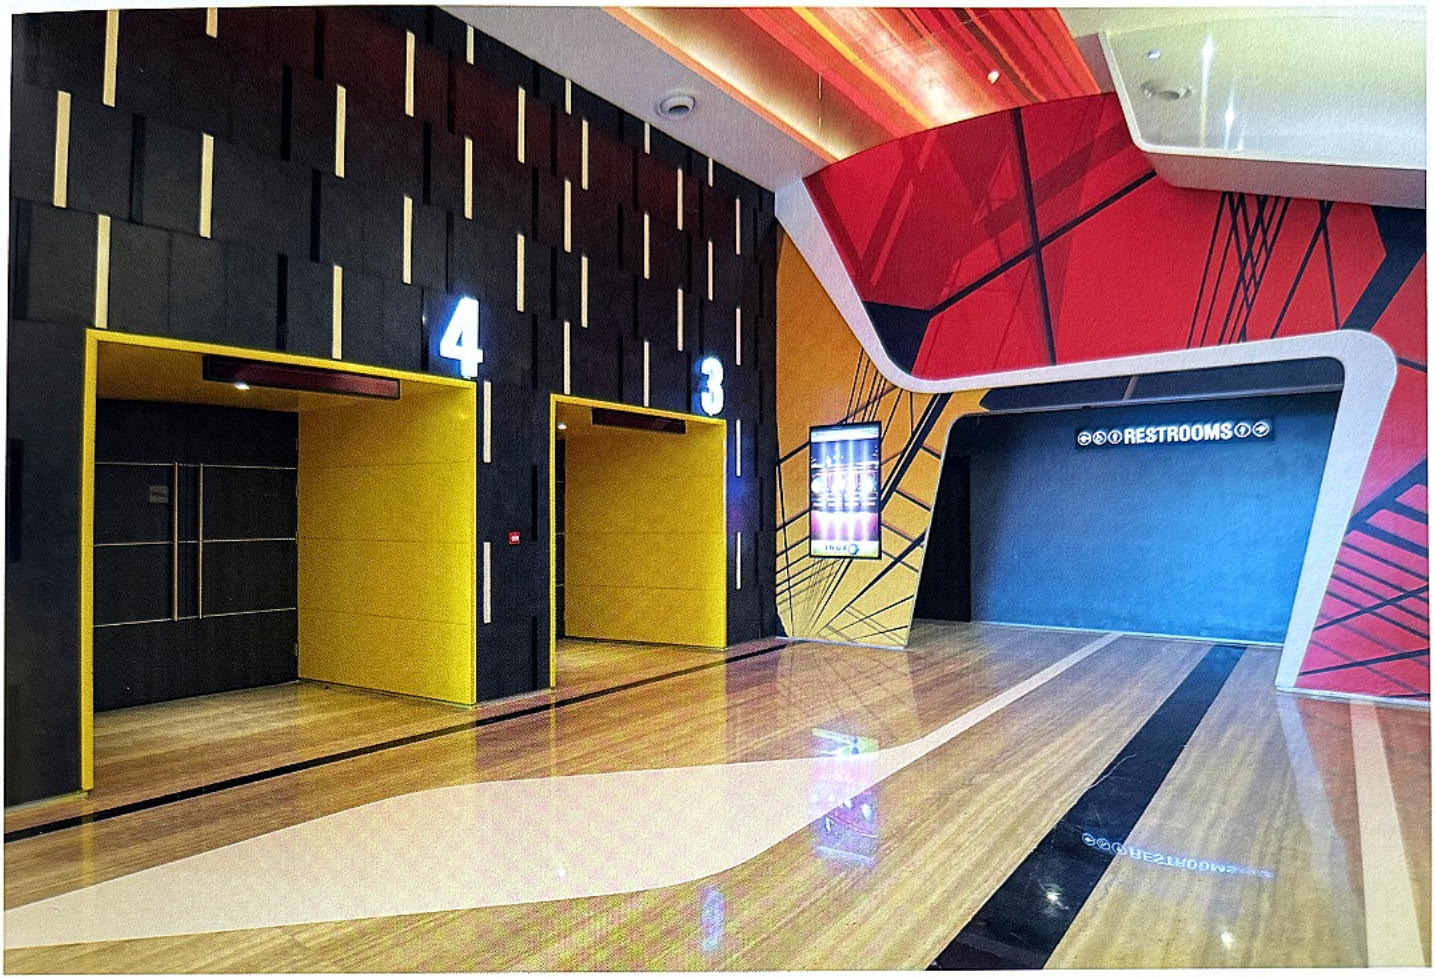
4
3
RESTROOMS

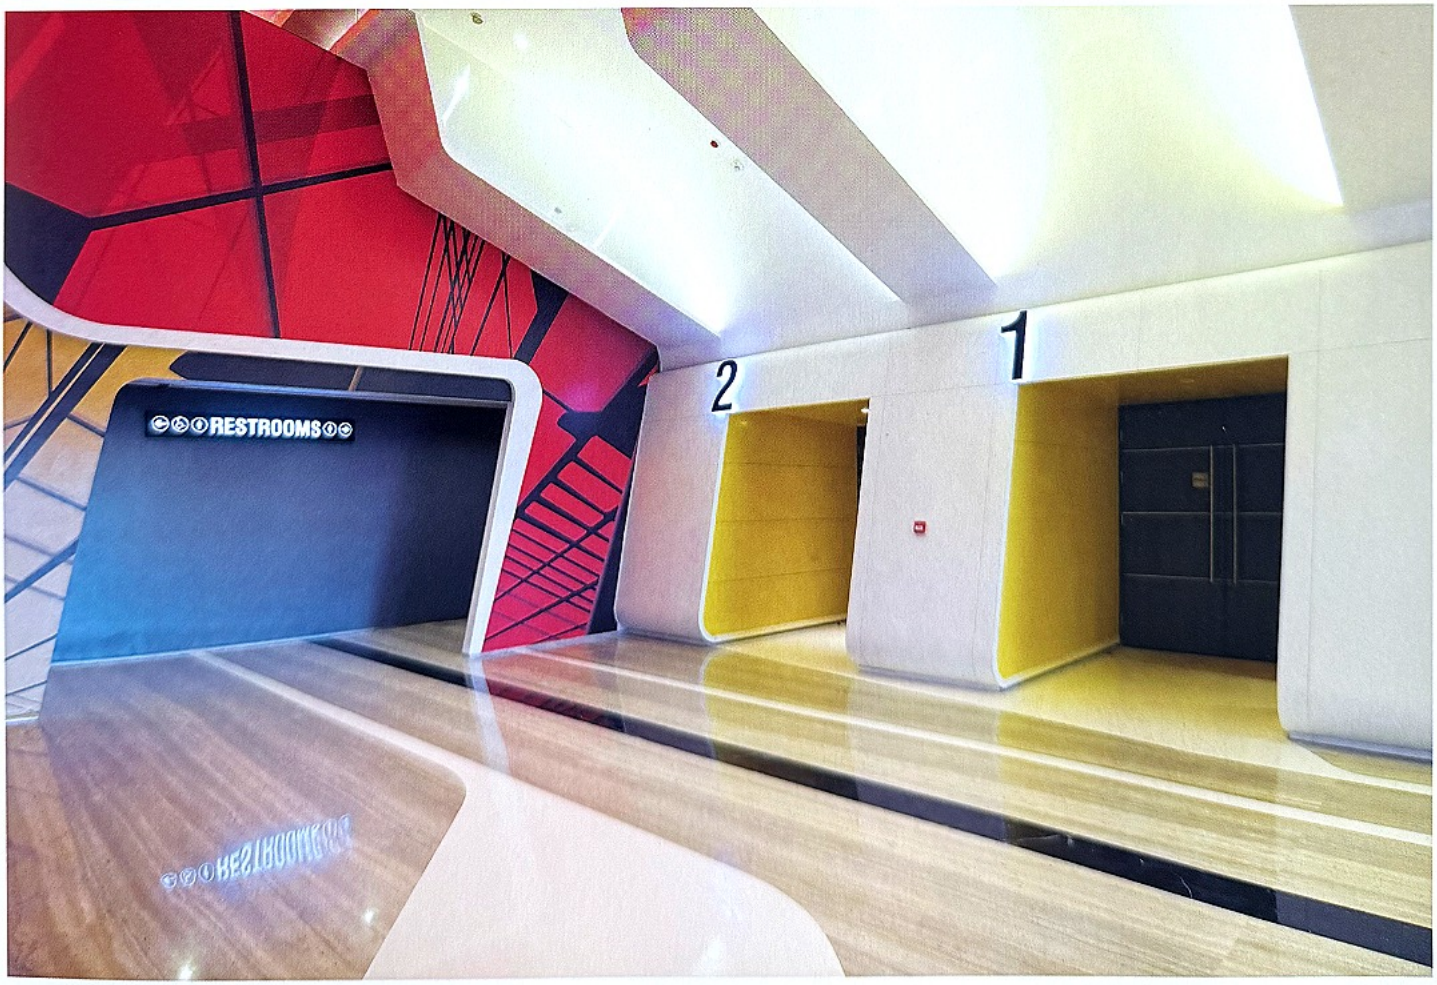
2
1
RESTROOMS

